
Commune de BLAYE LES MINES (81)

Chemin n°1

Réservoir de Bellevue

Plan d'Etat des Lieux

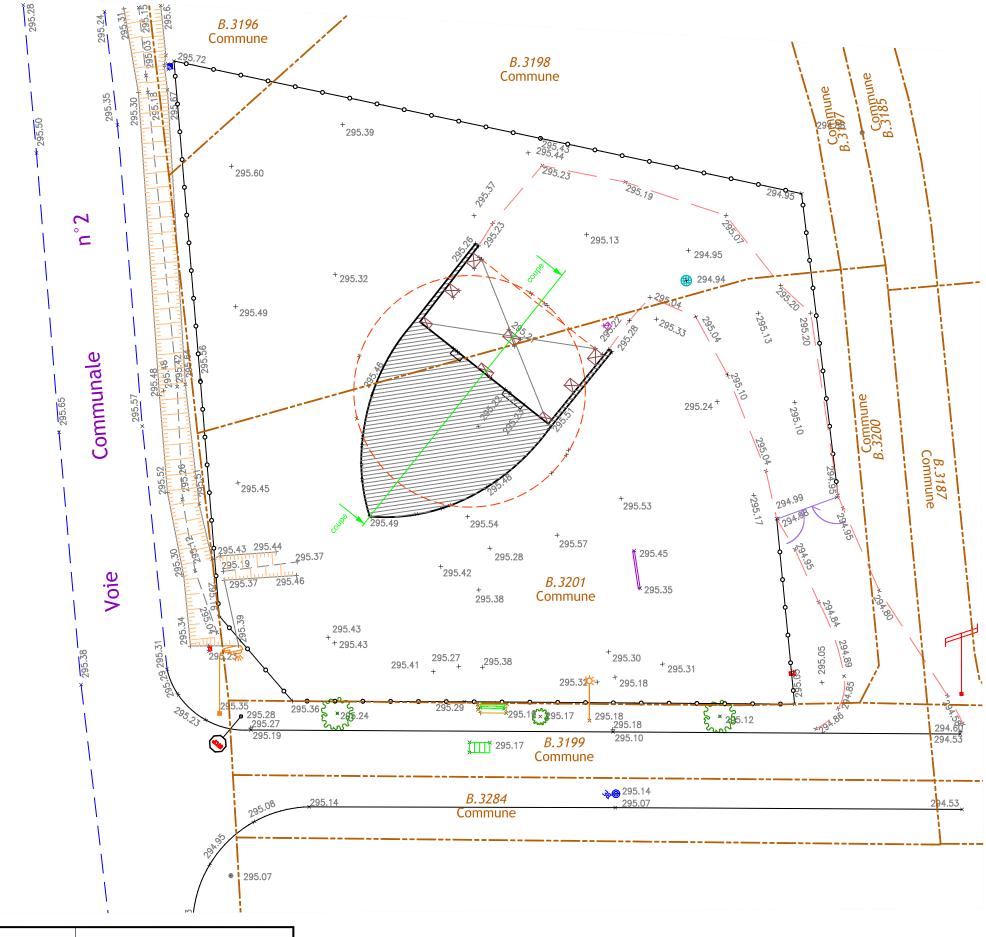



GéoSudOuest

___ Limite de propriété indicative

Application figurative du plan cadastral

(limites de propriétés non définies juridiquement)

Géomètre Expert : Lionel GUILLET (N°OGE : 04765)

Dossier : AL15038-18

Echelle 1/250

SARL de Géomètres Experts

Zac du Causse

81100 CASTRES

Tel: 05 63 59 17 60

castres@geo-sud-ouest.fr

Albi le 14/02/2018

28 Av Col. Teyssier 81000 ALBI Tel: 05 63 54 09 54 albi@geo-sud-ouest.fr

2 Rue Bertalaï 81200 MAZAMET Tel: 05 63 61 38 36 mazamet@geo-sud-ouest.fr

Rue Salvador Allende - Bât. H2 31320 CASTANET TOLOSAN Tel: 05 61 81 38 70 toulouse@geo-sud-ouest.fr

Ctre. d'Affaires St. Crescent 11100 NARBONNE Tel: 04 68 32 17 91 narbonne@geo-sud-ouest.fr

Place Compostelle 34330 LA SALVETAT/AGOUT Tel: 04 30 40 37 56 mazamet@geo-sud-ouest.fr

NOTA:

- Les coordonnées des points sont rattachées au système RGF 93 CC 44 et au NGF : origine TERIA